
※本書は重要事項説明書作成システムの動作検証用に作成した架空のサンプルです。実在の不動産・法人・個人とは一切関係ありません。

地 図 に 準 ず る 図 面 （ 公 図 ）

所在	大阪市西区北堀江三丁目	縮尺	1／500
種類	地図に準ずる図面（旧土地台帳附属地図）	作成年月日	令和8年9月24日　大阪法務局西出張所

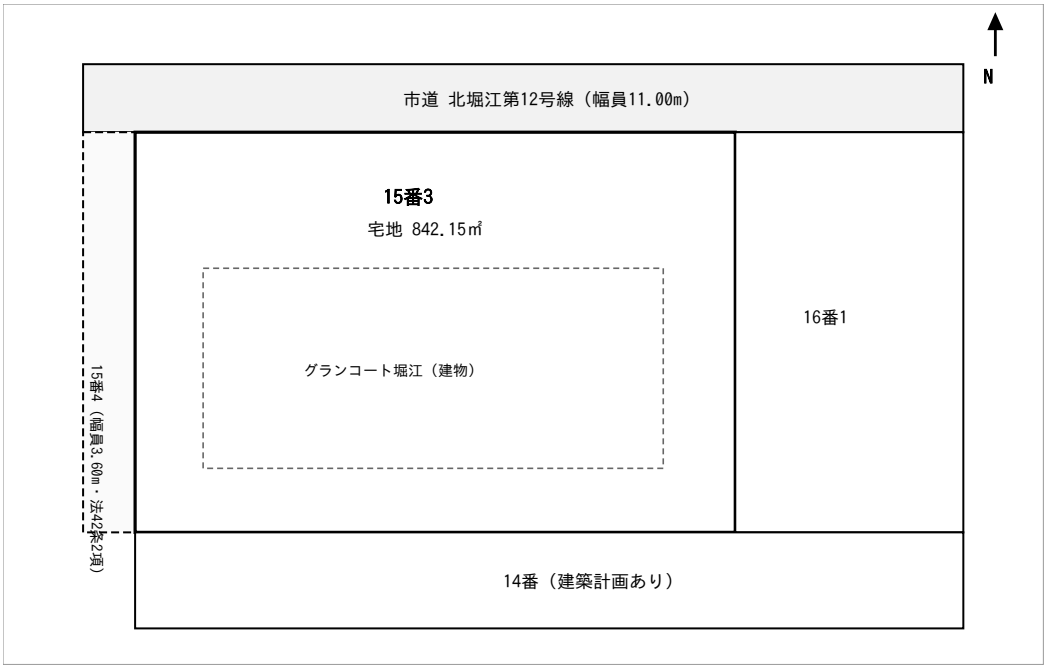


※ この図面は地図（不動産登記法第14条第1項）ではなく、地図に準ずる図面であるため、境界・形状・面積の正確性を保証するものではありません。

※ 15番4は、建物西側の通路部分であり、その全部が建築基準法第42条第2項道路（幅員3.60m）の区域に含まれます。


建 物 図 面

所在	大阪市西区北堀江三丁目15番地3、15番地4	縮尺	1／250
建物の名称	グランコート堀江	作成	昭和54年3月　土地家屋調査士 北堀　義行

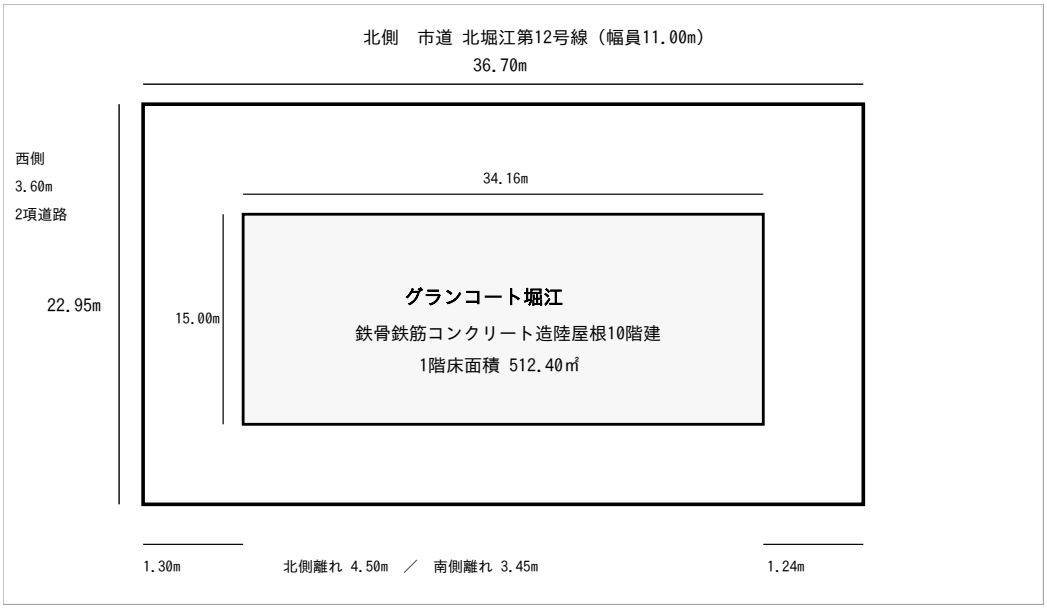

各 階 平 面 図 （ 5 階 ）

家屋番号	北堀江三丁目　15番3の506	縮尺	1／200
床面積	5階部分　62.35㎡（登記面積・内法）	壁芯面積	65.12㎡

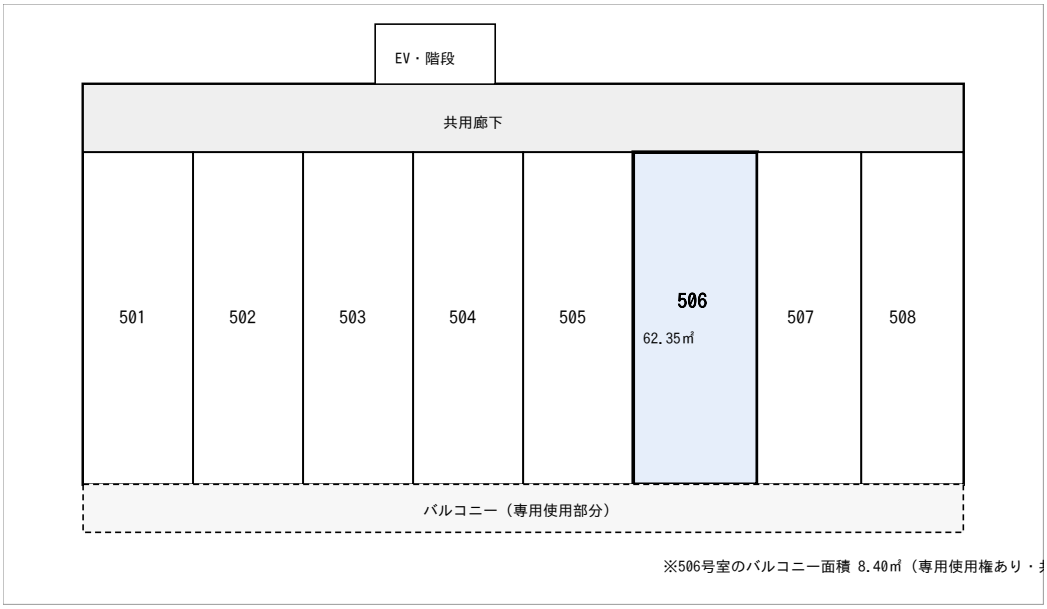

階	床面積（㎡）	住戸数	用途
1階	512.40	0	エントランスホール、管理員室、集会室（規約共用部分）、機械式駐車場、ごみ置場
2階～7階	各 628.15	各8戸（計48戸）	住戸
8階～9階	各 541.80	各7戸（計14戸）	住戸
10階	380.25	6戸	住戸、屋上塔屋（高置水槽）
合計	5,117.00	68戸	建築面積 512.40㎡／敷地面積（登記）1,050.72㎡

※ 登記床面積は内法（壁の内側）で算出、販売図面等の専有面積は壁芯で算出しているため相違があります。
※ バルコニー・玄関ポーチ・パイプスペースは共用部分であり、専有面積には含まれません。