
※本書は重要事項説明書作成システムの動作検証用に作成した架空のサンプルです。実在の不動産・法人・個人とは一切関係ありません。

地 図 （ 不 動 産 登 記 法 第 1 4 条 第 1 項 ）


所在	札幌市中央区伏見二丁目	縮尺	1／500
種類	**法第14条第1項の地図（国土調査成果）**	作成年月日	令和8年10月2日　札幌法務局

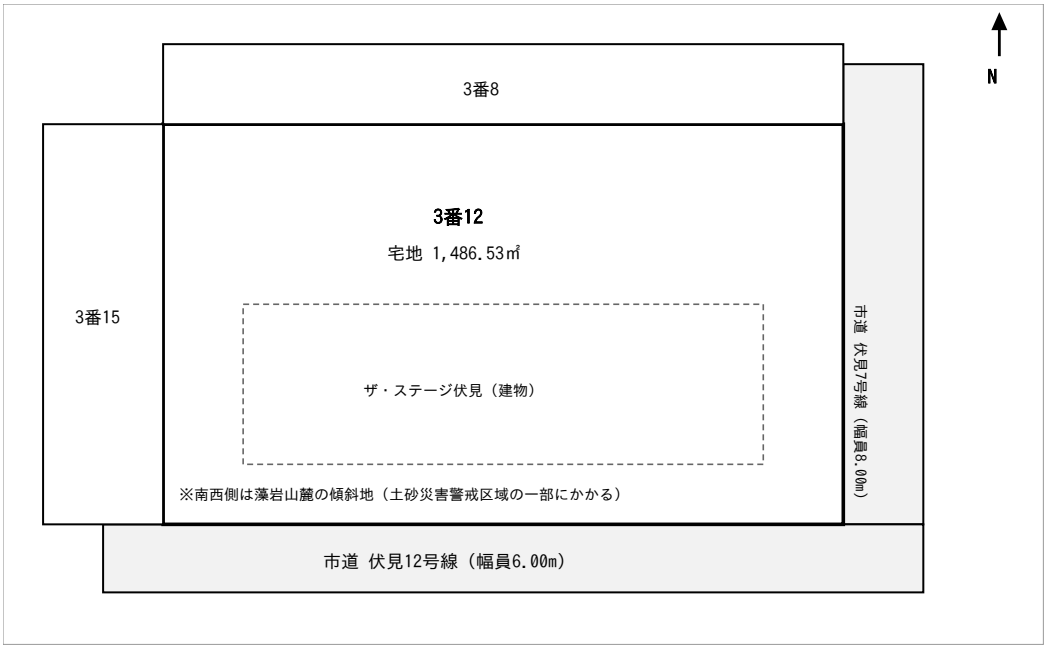

※ 本図は国土調査による成果であり、不動産登記法第14条第1項の地図（精度区分 甲二）です。 地積測量図と併せて境界の確認が可能です。

建 物 図 面


所在	札幌市中央区伏見二丁目3番地12	縮尺	1／250
建物の名称	ザ・ステージ伏見	作成	平成17年11月　土地家屋調査士　円山　達哉

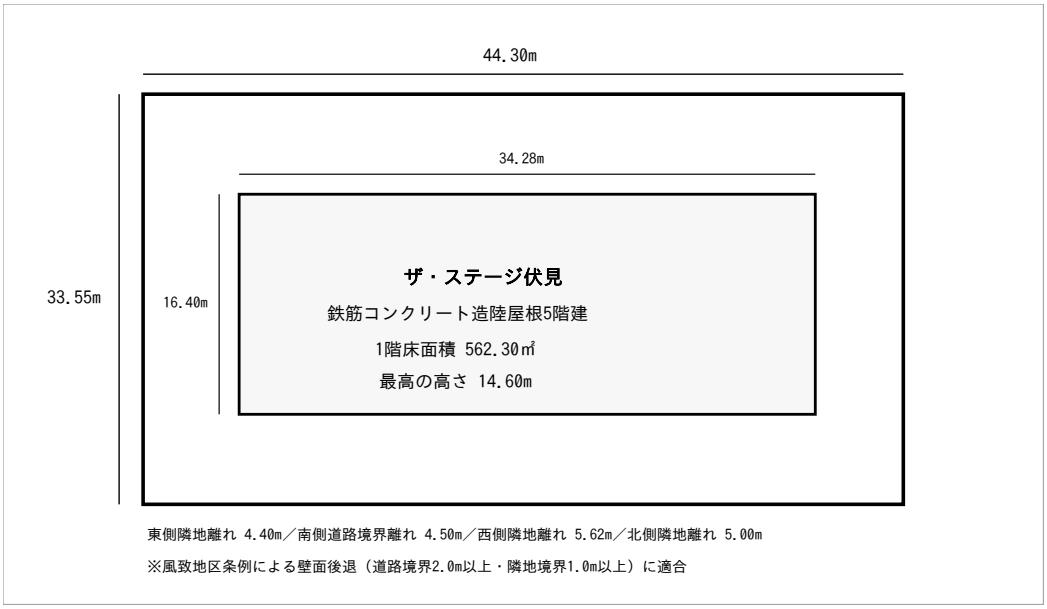

敷地面積	1,486.53㎡	建築面積	562.30㎡
建ぺい率	**37.83%（指定60%・風致地区40%以下に適合）**	延べ面積	2,624.60㎡
容積率	**176.55%（指定200%に適合）**	最高の高さ	**14.60m（風致地区15m以下に適合）**
緑化面積	312.40㎡（緑化率 21.0%・風致地区20%以上に適合）	既存不適格	**該当なし**

各 階 平 面 図 （ 5 階 ）

家屋番号	伏見二丁目　3番12の503	縮尺	1／200
床面積	5階部分　78.92㎡（登記面積・内法）	壁芯面積	81.36㎡

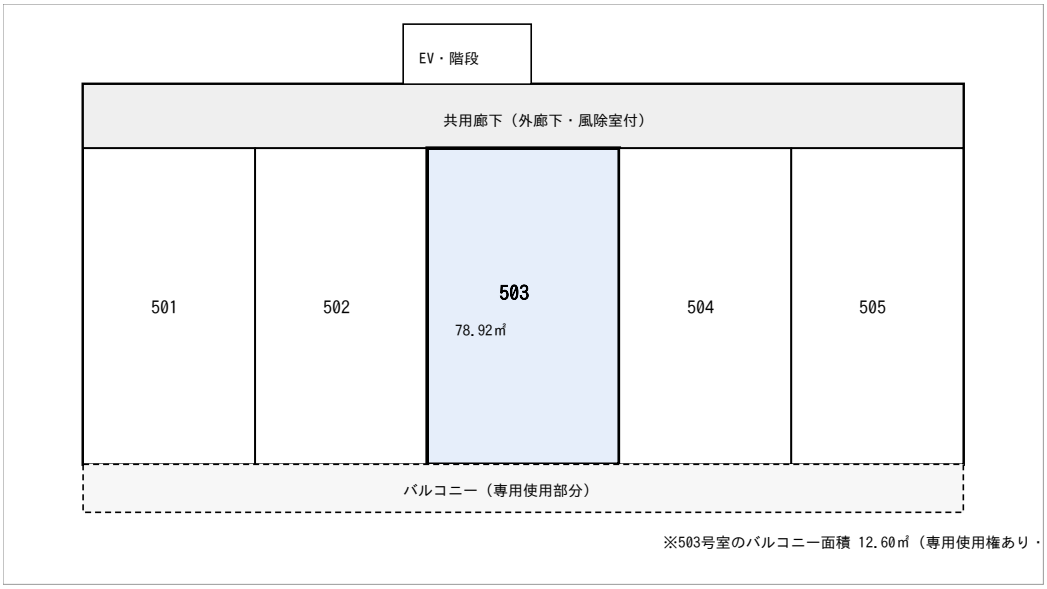

階	床面積（㎡）	住戸数	用途
1階	562.30	4	住戸、エントランス（風除室）、管理員室、集会室、トランクルーム、ごみ置場
2階～4階	各 540.80	各7戸（計21戸）	住戸
5階	439.90	5戸	住戸、屋上塔屋
合計	2,624.60	30戸	建築面積 562.30㎡／敷地面積 1,486.53㎡

※ 登記床面積は内法、販売図面等の専有面積は壁芯で算出しているため相違があります。
※ 多雪区域（垂直積雪量1.4m）のため、屋上及びバルコニーには積雪荷重を考慮した構造としています。 バルコニーでの雪下ろし作業は落雪事故防止のため禁止されています（使用細則）。